



KATAHDIN CEDAR LOG HOME DESIGNED FOR:


STEPHEN & JULIE FORRESTAL

PLAN #: 01043803

SHEET 1 OF 6

#1: CEDAR LOG INFORMATION

A: SIZE: 6" WIDE x 8" TALL

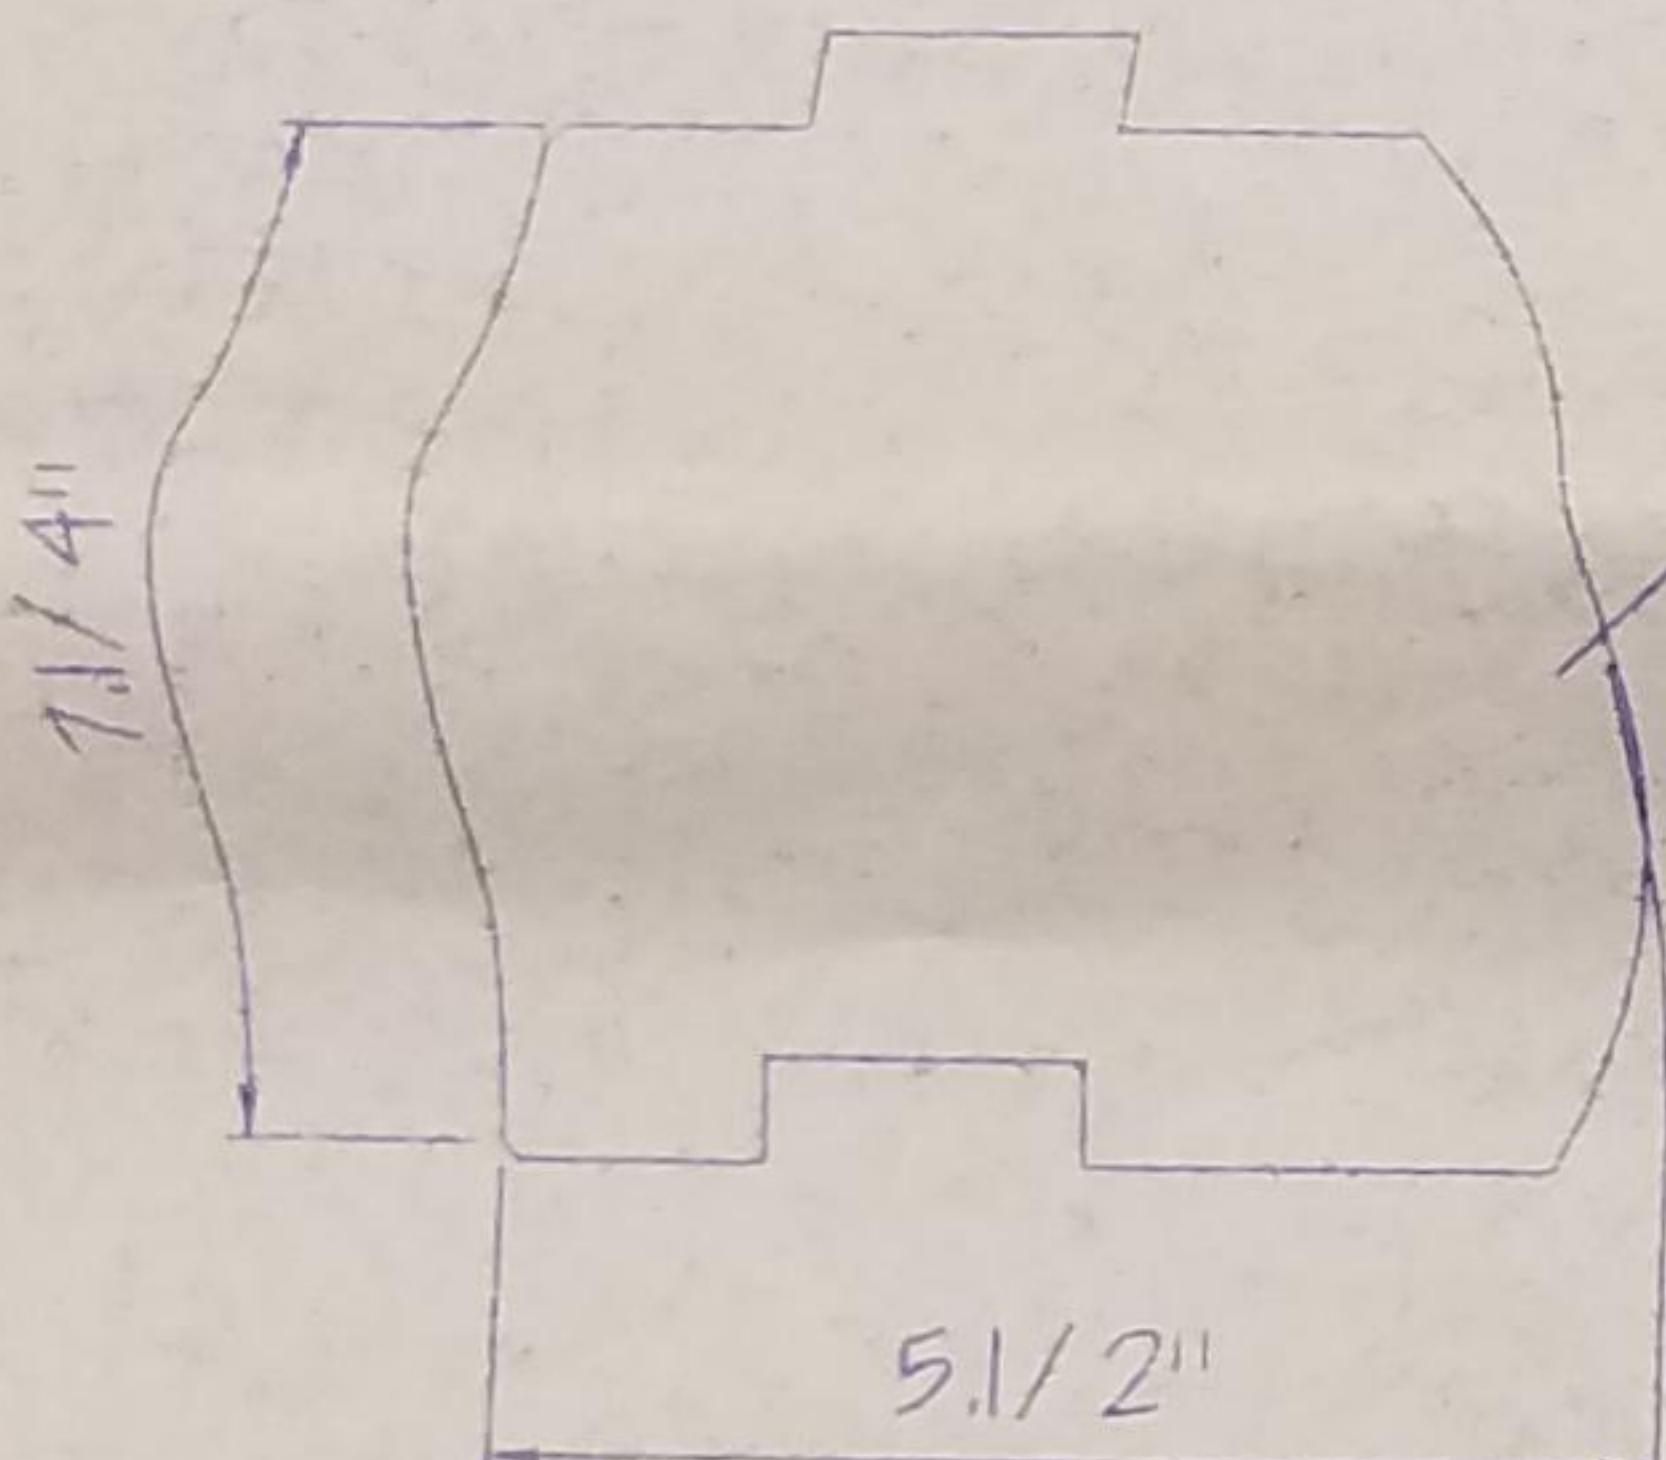

B: EXT. FACE FINISH:
HANDPEELED

C: GRADE: #1 PREMIUM

D: CORNER STYLE: BUTT AND PASS

You can make a custom wall using this profile, similar to this video:
<https://youtu.be/JeUmQm0lBww?t=986>

CUSTOMER NOTICE

THESE PLANS ARE PROVIDED FOR YOUR APPROVAL AND / OR REVISIONS. PLEASE REVIEW THESE PLANS THOROUGHLY AND SIGN IN THE SPACE PROVIDED BELOW WITH ANY NOTATIONS REQUIRED. SIGNATURE OF APPROVAL MUST BE RECEIVED BY KATAHDIN FOREST PRODUCTS BEFORE ANY ADDITIONAL DRAWINGS CAN BE PROVIDED. AFTER APPROVAL DRAWINGS ARE SIGNED CHANGES OR MODIFICATIONS WILL BE AT ADDITIONAL COST.

#2 WINDOW & EXT DOOR INFORMATION

A: MANUFACTURER: BY OWNER

B: COLOR: BY OWNER

C: WINDOW SCHEDULE (@ LOG WALLS ONLY)

QTY.	MFG. #	DESCRIPTION	SIZE LISTED ON PLAN	ROUGH OPENING (W x H)
3		DOUBLE HUNG	5'-7 3/4" x 4'-9 1/4"	5'-8" x 4'-9 1/4"
2		DOUBLE HUNG	5'-7 3/4" x 3'-5 1/4"	5'-8" x 3'-5 1/4"
1		DOUBLE HUNG	4'-3 1/2" x 4'-1 1/4"	4'-4" x 4'-1 1/4"
1		DOUBLE HUNG	2'-10 1/8" x 4'-9 1/4"	2'-10 1/2" x 4'-9 1/4"
2		DOUBLE HUNG	2'-6 1/8" x 4'-9 1/4"	2'-6 1/2" x 4'-9 1/4"
1		DOUBLE HUNG	2'-6 1/8" x 4'-1 1/4"	2'-6 1/2" x 4'-1 1/4"
1		DOUBLE HUNG	2'-2 5/8" x 4'-1 1/4"	2'-3" x 4'-1 1/4"
1		DOUBLE HUNG	2'-2 1/8" x 3'-5 1/4"	2'-2 1/2" x 3'-5 1/4"
1	3/0X6/8 W 12" SIDELIGHTS	THERMA-TRU EXT DOOR	63 3/4" x 82 1/2"	64 1/2" x 82 1/2"
1	2/8-6/8	THERMA-TRU EXT DOOR	2'-9 5/8" x 6'-10"	2'-10 1/2" x 6'-10 1/2"
1	PNG 6068	ANDERSEN SLIDING DOOR	5'-11 1/4" x 6'-7 1/2"	6'-0 1/2" x 6'-8 1/2"
2	PNG 8068	ANDERSEN SLIDING DOOR	7'-11 1/4" x 6'-7 1/2"	8'-0 1/2" x 6'-8 1/2"

APPROVED WITHOUT MODIFICATIONS

APPROVED BY _____

DATE _____

#4: PLAN APPROVAL

APPROVED WITH NOTED CHANGES

IT IS UNDERSTOOD THAT CHANGES NOTED MAY REQUIRE STRUCTURAL OR AESTHETIC MODIFICATIONS TO THIS BUILDING


APPROVED BY _____

DATE _____


REV

(NO S

OIO

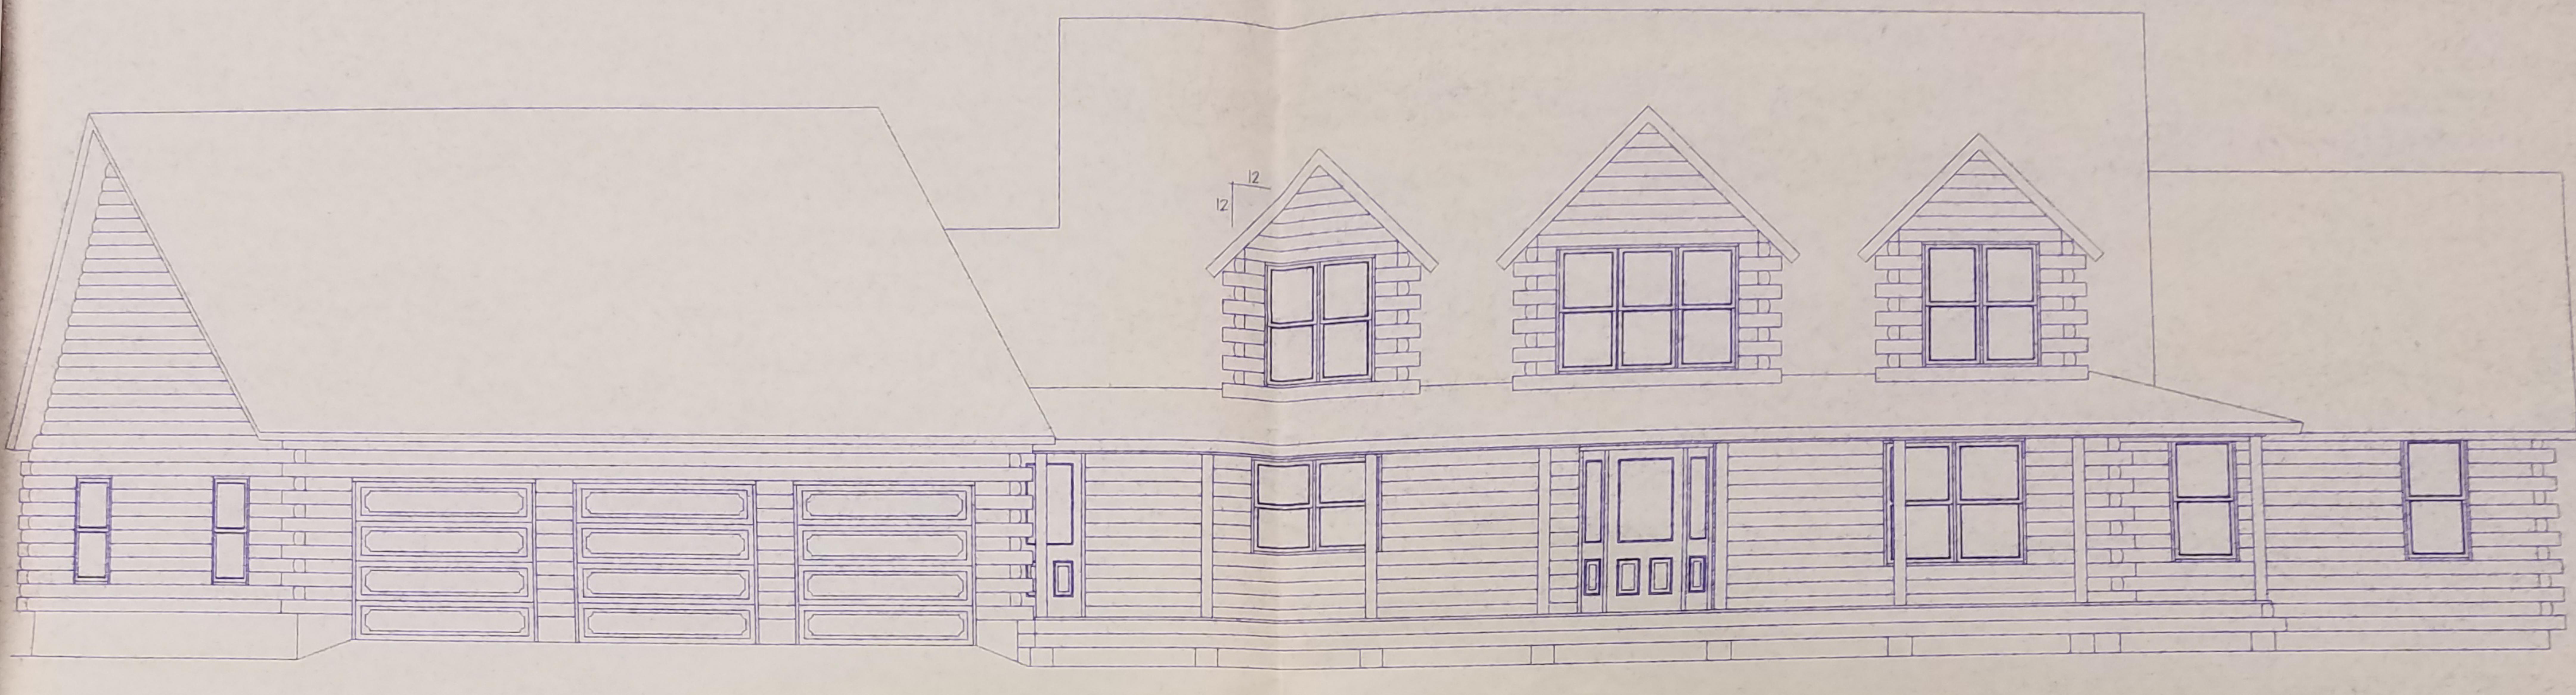

FRONT ELEVATION

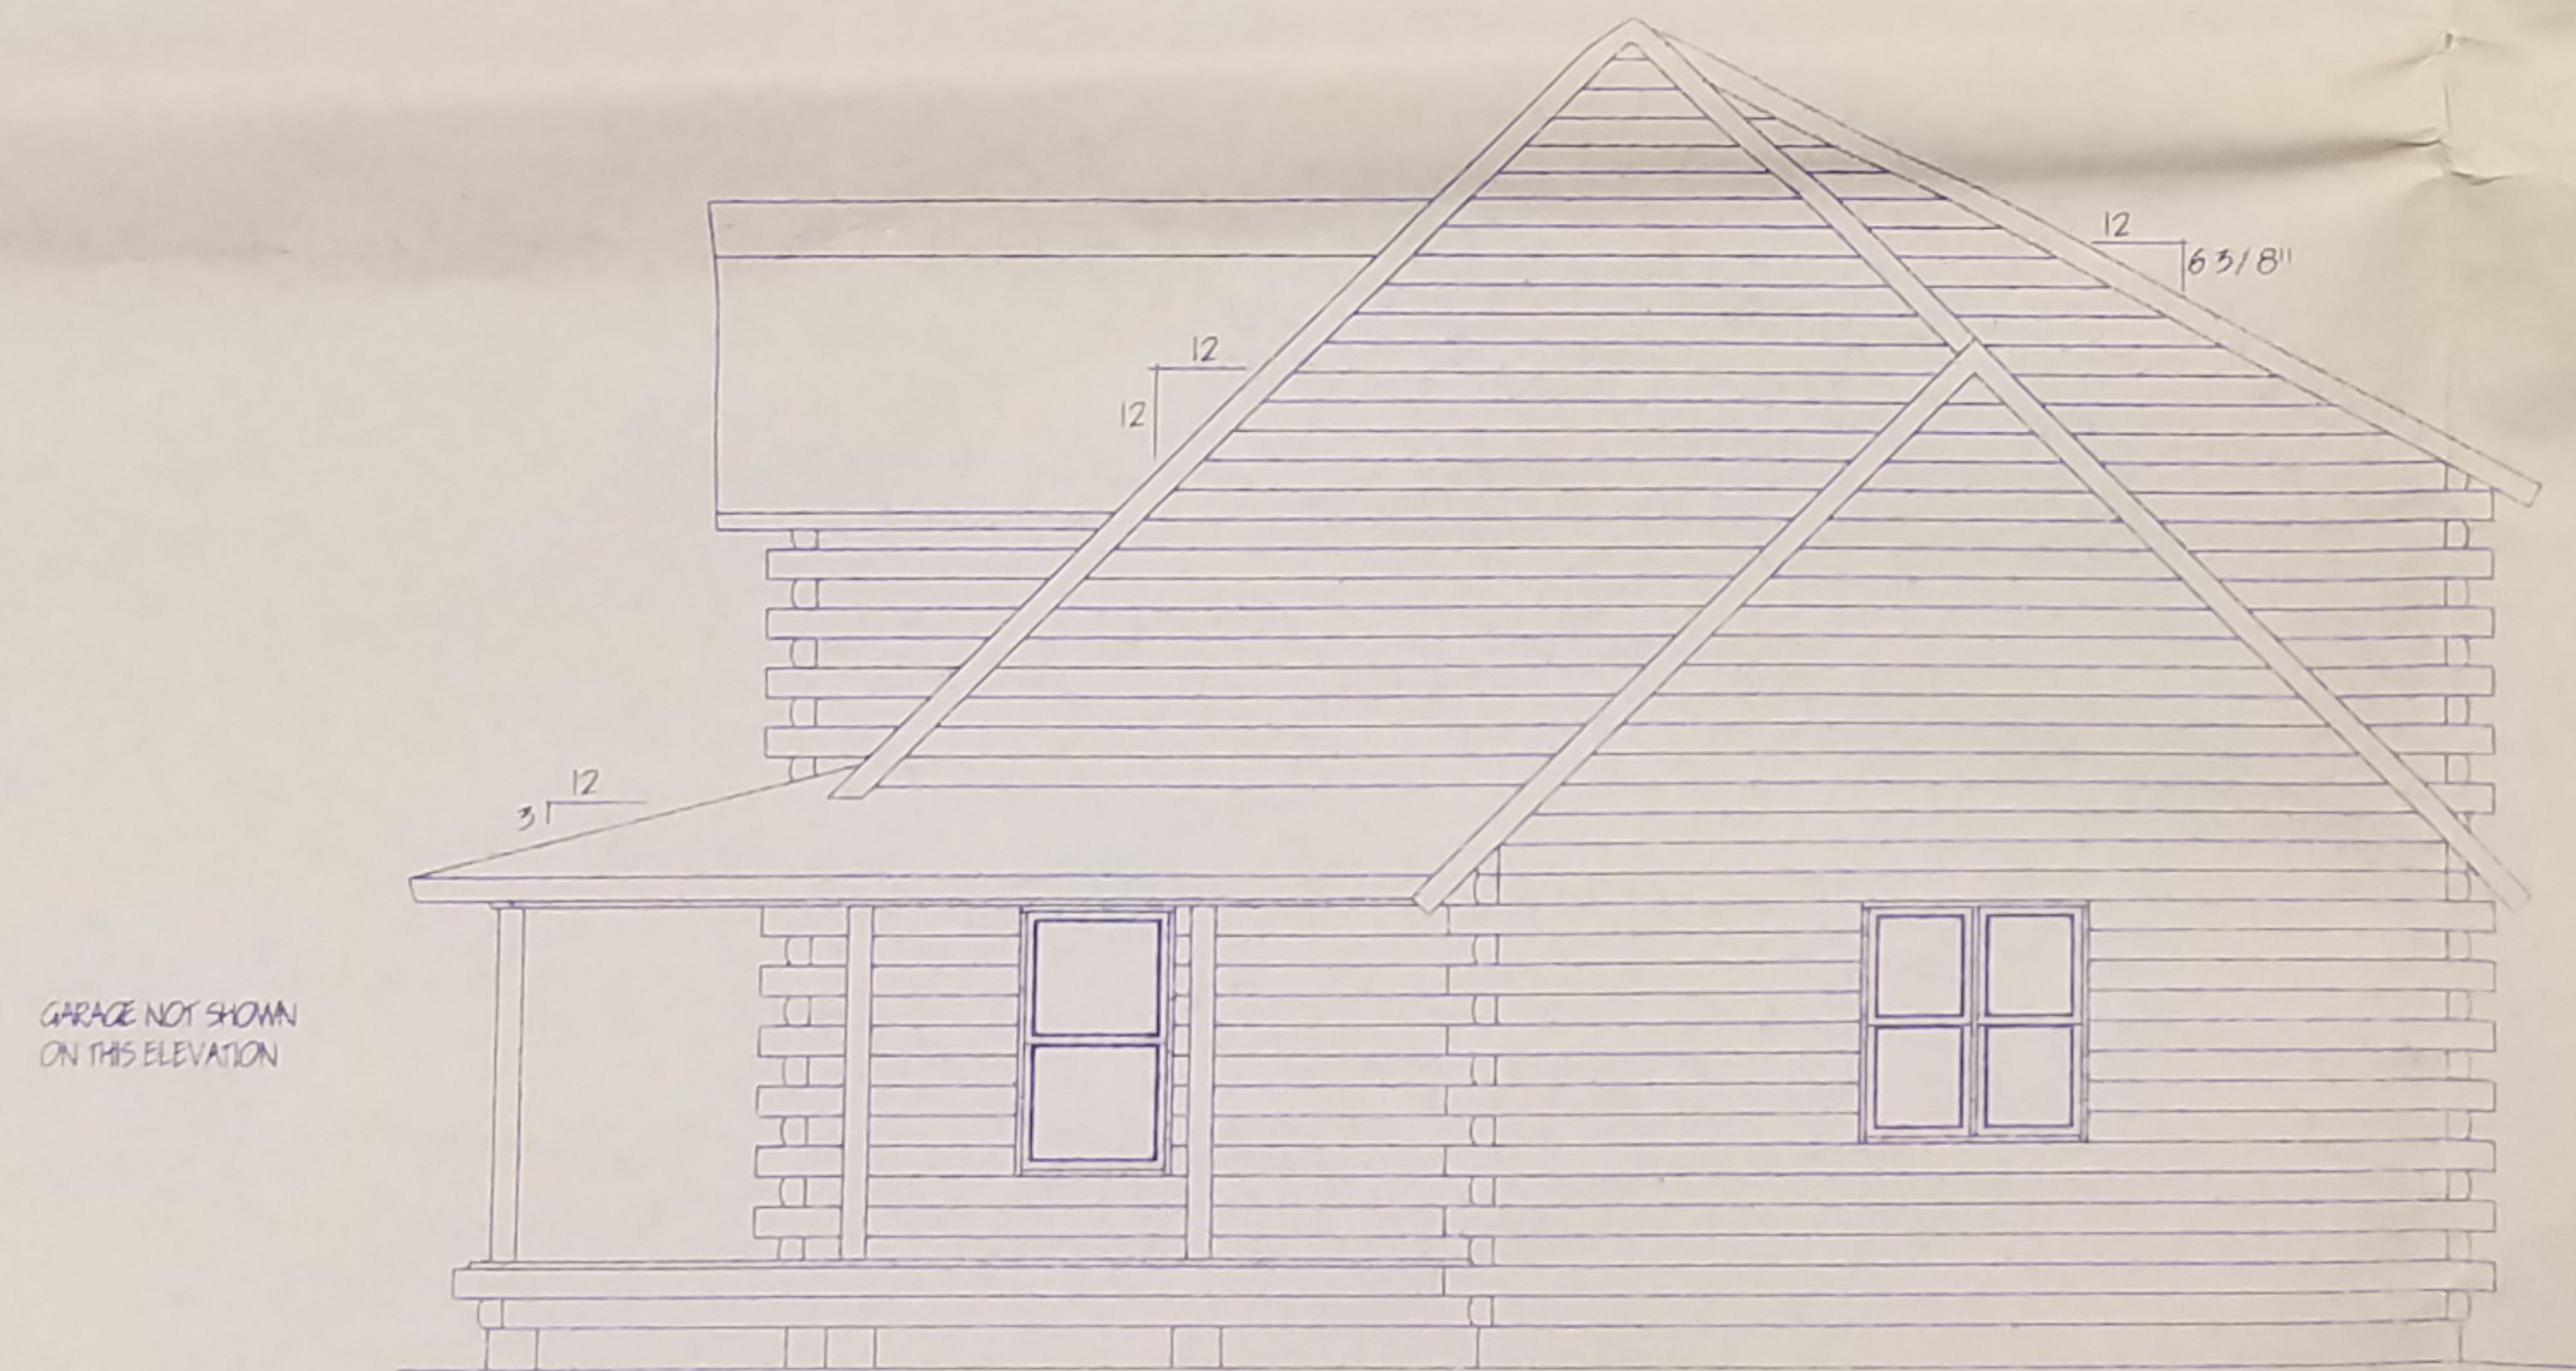


RIGHT ELEVATION

NOTE:
RUSTIC RAIL ON PORCH NOT SHOWN FOR CLARITY

LOGS TO BE 8" HEIGHT (14 ROWS)
ALL GABLES AND DORMERS TO BE PRIMED
AND COVERED WITH LOG SIDING


 <p>KATAHDIN cedar log homes</p> <p>KATAHDIN FOREST PRODUCTS PO BOX #145 OAKFIELD, ME 04763 1-800-845-4933 FAX 1-207-757-8268</p>		<p><u>PLAN APPROVAL</u></p> <p><input type="checkbox"/> APPROVED WITHOUT ANY MODIFICATIONS APPROVED BY _____ DATE _____</p> <p>LOG STYLE (check one)</p> <p><input type="checkbox"/> C1 (HAND PEELED CEDAR) <input type="checkbox"/> C2 (MILLED CEDAR) <input type="checkbox"/> P1 (MILLED PINE) <input type="checkbox"/> OTHER _____</p>	<p><u>CUSTOMER NOTICE</u></p> <p>THESE PLANS ARE PROVIDED FOR YOUR APPROVAL AND / OR REVISIONS. PLEASE REVIEW THESE PLANS THOROUGHLY AND SIGN IN THE SPACE PROVIDED ABOVE WITH ANY NOTATIONS REQUIRED. SIGNATURE OF APPROVAL MUST BE RECEIVED BY KATAHDIN FOREST PRODUCTS BEFORE ANY ADDITIONAL DRAWINGS CAN BE PROVIDED.</p> <p>AFTER APPROVAL DRAWINGS ARE SIGNED, CHANGES OR MODIFICATIONS WILL BE AT ADDITIONAL COST.</p>	<p><u>CUSTOMER:</u> STEPHEN & JULIE FORRESTAL</p> <p><u>TITLE:</u> ELEVATIONS</p> <p><u>DATE:</u> 4-17-01</p> <p><u>DRN BY:</u> DEH</p> <p><u>SCALE:</u> 3/16"=1'-0"</p> <p><u>PLAN #:</u> 01043803</p>
---	--	---	---	---

 

PLAN APPROVAL	
<input type="checkbox"/> APPROVED WITHOUT ANY MODIFICATIONS	APPROVED BY _____
DATE _____	
LOG STYLE (check one)	
<input type="checkbox"/> C1 (HAND PEELED CEDAR)	<input type="checkbox"/> C2 (MILLED CEDAR)
<input type="checkbox"/> P1 (MILLED PINE)	<input type="checkbox"/> OTHER _____

CUSTOMER NOTICE
 THESE PLANS ARE PROVIDED FOR YOUR APPROVAL AND / OR REVISIONS. PLEASE REVIEW THESE PLANS THOROUGHLY AND SIGN IN THE SPACE PROVIDED ABOVE WITH ANY NOTATIONS REQUIRED. SIGNATURE OF APPROVAL MUST BE RECEIVED BY KATAHDIN FOREST PRODUCTS BEFORE ANY ADDITIONAL DRAWINGS CAN BE PROVIDED. AFTER APPROVAL DRAWINGS ARE SIGNED CHANGES OR MODIFICATIONS WILL BE AT ADDITIONAL COST.

CUSTOMER: STEPHEN & JULIE FORRESTAL	SCALE: 3/16" = 1'-0"
TITLE: FLOOR PLAN	
DATE: 4-17-01	
DRN BY: DEH	SHEET 3 OF 6
PLAN # 01043803	

 

LOFT PLAN

NOTE
REFER TO ARCHITECTURAL PLAN FOR LOFT ROOM LAYOUT

CUSTOMER
STEPHEN & JULIE FO
TITLE:
LOFT PLAN
DATE:
4-17-01

TOP ROW TO BE TRUSS PLATE, TYP.

• O1 7'-3" (PTP)	• O2 4'-5" (PTP)	• O3 8'-11 1/2" (PTP)	• O4 6'-9" (PTP)	• O5 8'-8" (PTP)	• O6 4'-2 1/4" (PTP)	• O7 8'-11 1/2" (PTP)	• O8 4'-10" (PTP)
• N1 6'-9" (K)	N2 5'-5"	• N3 7'-11 1/2" (K)	N4 6'-9"	• N5 7'-8" (K)	N6 5'-2 1/4"	• N7 7'-11 1/2" (K)	N8 5'-10"
M1 2'-7"	M2 7'-5"	L2 7'-5"	M3 6'-0"	I3 2'-6"	I4 6'-3"	M5 7'-2 1/4"	M6 3'-7 1/8" ()
K1 2'-7"	K2 7'-5"	J2 7'-5"	K3 3'-6"	J3 5'-0"	J4 3'-3"	L5 7'-2 1/4"	L6 4'-6"
H1 2'-7"	H2 7'-5"	F1 2'-7"	G2 7'-5"	H3 4'-0"	H4 4'-9"	K5 7'-2 1/4"	K6 3'-7 1/8" ()
G1 2'-7"	E2 6'-5"	D2 5'-0"	E3 7'-11 1/2"	G3 3'-0"	G4 5'-9"	J6 7'-2 1/4"	J8 4'-6"
E1 2'-7"	C2 4'-0"	D3 7'-0"	E4 7'-9"	F3 6'-0"	F4 2'-9"	H5 7'-2 1/4"	H6 3'-7 1/8" ()
D1 2'-7"	B2 8'-0"	C3 6'-0"	D4 6'-0"	D5 4'-1 1/2"	C6 6'-2 1/4"	F5 7'-2 1/4"	F6 4'-6"
C1 2'-7"	A1 2'-7" (XX)	B1 2'-7"	A2 6'-0" (XX)	B2 8'-0"	B3 8'-0"	E5 7'-2 1/4"	E6 3'-7 1/8" ()
B1 2'-7"	A3 6'-0" (XX)	A4 6'-0" (XX)	A5 4'-1 1/2" (XX)	A6 6'-0" (XX)	A7 6'-0" (XX)	D6 7'-2 1/4"	D7 3'-7 1/8" ()

6" added to the length of these logs (CUT IN FIELD)

3/0-6/8 w/ SIDELITES

6x6 INSIDE CORNER POST

w/ 2x4 STUDS, SHEATHED, & COVERED w/ LOG SIDING

ELEVATION "A"

12

12

3 required

GABLE ENDS TO BE FRAMED
w/ 2x4 STUDS, SHEATHED, AND
COVERED w/ T&G LOG SIDING.

• O9 2'-10 1/8" (PTP)	• O10 6'-2" (PTP)	• O11 4'-7 1/2" (PTP)
(M9 3'-4 1/8")	(N10 5'-2" (K))	(N11 5'-1 1/2")
M7 5'-3"	M8 6'-1 1/2"	L8 6'-1 1/2"
L7 4'-4 1/8"	K7 5'-3"	K8 6'-1 1/2"
J7 4'-4 1/8"	H8 6'-1 1/2"	J8 6'-1 1/2"
H7 5'-3"	G8 6'-1 1/2"	G9 6'-1 1/2"
G7 4'-4 1/8"	F8 6'-1 1/2"	F9 2'-1"
F7 5'-3"	E8 6'-1 1/2"	F10 7'-0 1/2"
E7 4'-4 1/8"	D9 6'-1 1/2"	F11 7'-0 1/2"
D8 5'-3"	C10 5'-2"	D11 7'-0 1/2"
C9 3'-4 1/8"	B10 8'-0"	D12 2'-1 1/2"
B10 8'-0"	A10 7'-5 1/8" (XX)	C13 4'-10"
A9 6'-0" (XX)		

6x6 INSIDE CORNER POST

ELEVATION "B"

2 extra rows @ master bedroom wing.
adjust height of plate cut in field to match
main house roof.

• Q1 8'-0" (PTP)	• Q2 6'-0" (PTP)	• Q3 6'-0" (PTP)
P1 6'-4 1/2"	P2 5'-0 1/2"	P3 8'-1"
D12 2'-1" * N13 2'-10"	Q14 7'-0 1/2"	O15 2'-10 1/2" 2'-10 1/8" ()
N12 1'-1"	N14 5'-0 1/2"	N16 2'-9"
M9 2'-1"	M10 7'-0 1/2"	M11 2'-10 1/8" ()
L9 2'-1"	L10 7'-0 1/2"	L11 3'-9"
K9 2'-1"	K10 7'-0 1/2"	K11 2'-10 1/8" ()
J9 2'-1"	J10 7'-0 1/2"	J11 3'-9"
H9 2'-1"	H10 7'-0 1/2"	H11 2'-10 1/8" ()
G9 2'-1"	G10 7'-0 1/2"	G11 3'-9"
F9 2'-1"	F10 7'-0 1/2"	F11 2'-10 1/8" ()
E9 2'-1"	E10 7'-0 1/2"	E11 3'-9"
D10 2'-1"	D11 7'-0 1/2"	D12 2'-10 1/8" ()
C12 1'-1"	C13 4'-10"	C14 5'-0 1/2"
B10 8'-0"	B11 6'-0"	C15 4'-10" C16 2'-9"
A11 6'-0" (XX)	A12 6'-0" (XX)	B12 3'-7 5/8" ()
		A13 5'-6 1/2" (XX)

ELEVATION "C"



APPRO
APPRO

LOG
LOG

CU
THESE PLAN
AND / OR
PLANS THO
PROVIDED A
SIGNATURE
KATAHDIN PC
ADDITIONAL
CHANGES OR
ADDITIONAL
CUSTOMER

TITLE:
LOC

DATE:
5-1-01

DRAW BY:
HL

PLAN #:
010

2 extra rows @ master bedroom wing
adjust height of plate cut in field to match
main house roof.

• Q8 6'-0" (PTP)		• Q9 8'-0" (PTP)		• Q10 6'-0" (PTP)
P7 3'-11"	P8 4'-6 1/2"	P9 3'-0"		P10 8'-0 1/2"
(O20 3'-6 1/8"	O21 7'-6 1/2"	N22 3'-0"		O22 6'-4"
N20 3'-5"	• N21 4'-6 1/2" (K)	M15 5'-0"		• N23 8'-4" (K)
(N14 3'-6 1/8"		L15 5'-0"		
L14 4'-5"		K15 5'-0"		
(K14 3'-6 1/8"		J15 5'-0"		
J14 4'-5"		H15 5'-0"		
(H14 3'-6 1/8"		G15 5'-0"		
G14 4'-5"		F15 5'-0"		
(F14 3'-6 1/8"		E15 5'-0"		
E14 4'-5"		D18 4'-0"		
(D15 2'-6 1/8"	D17 4'-6 1/2"	C21 4'-11 1/2"		FWG 6068
C20 7'-0"		B18 7'-6 5/8"		
(B17 3'-6"		A18 5'-11 1/2" (YX)		
• A17 6'-0" (XX)				

FWG 6

DORMERS TO BE FRAMED
W/ 2x4 STUDS, SHEATHED,
& COVERED W/ LOG SIDING

• COVERED w/											
023 5'-0 1/2" (PTP)		024 7'-9" (PTP)		025 7'-11 1/2" (PTP)		026 2'-5 1/4"					
N24 4'-6 1/2"		N25 4'-10" (K)		N26 2'-11"		N27 7'-11 1/2" (K)		N28 1'-5 1/4"			
M16 6'-6 1/2"				M17 4'-11"				M18 3'-5 1/4"			
L16 6'-6 1/2"				L17 4'-11"				L18 3'-5 1/4"			
K16 6'-6 1/2"				K17 4'-11"				K18 3'-5 1/4"			
J16 6'-6 1/2"			2'-6 1/8" x 4'-1 1/4"	J17 4'-11"			5'-7 3/4" x 4'-9 1/4"	J18 3'-5 1/4"			
H16 6'-6 1/2"				H17 4'-11"				H18 3'-5 1/4"			
G16 6'-6 1/2"				G17 4'-11"				G18 3'-5 1/4"			
F16 6'-6 1/2"				F17 4'-11"				F18 3'-5 1/4"			
E16 6'-6 1/2"				E17 4'-11"				E18 3'-5 1/4"			
D19 5'-6 1/2"		020 4'-10"		D21 3'-11"				D22 3'-5 1/4"			
C22 7'-0"			C23 6'-3 1/2"				C24 7'-11 1/2"		C25 2'-5 1/4"		
B19 8'-0"			B20 4'-0"				B21 6'-0"		B22 5'-8 1/4"		
A19 4'-0" (XX)		• A20 6'-0" (XX)		• A21 6'-0" (XX)				• A22 7'-8 1/4" (XX)			

FWG 80

• 028	2'-5 1/4" (PTP)	029	6'-11 1/2" (PTP)	• 030	4'-2 1/2" (PTP)
N30	1'-5 1/4"	• N31	7'-11 1/2" (K)	N32	3'-2 1/2"
M19	3'-5 1/4"			L20	2'-9 5/8")
I19	3'-5 1/4"			L20	3'-8 1/2")
K19	3'-5 1/4"			K20	2'-9 5/8")
J19	3'-5 1/4"			J20	3'-8 1/2")
H19	3'-5 1/4"	5'-7 3/4" x 4'-9 1/4"		H20	2'-9 5/8")
G19	3'-5 1/4"			G20	3'-8 1/2")
F19	3'-5 1/4"			F20	2'-9 5/8")
E19	3'-5 1/4"			E20	3'-8 1/2")
D23	3'-5 1/4"			D24	2'-9 5/8")
C26	2'-5 1/4"	C27	7'-11 1/2"	C28	2'-8 1/2")
	B23	8'-0"		B24	4'-2 3/8")
• A23	6'-0" (XX)		• A24	7'-1 1/4" (XX)	

ELEVATION "E"

model
this area.

GABLE ENDS TO BE FRAMED
w/ 2x4 STUDS, SHEATHED, AND
COVERED w/ T&G LOG SIDING

• 031 4'-0" (PTP)	• 032 9'-6 1/8" (PTP)	• 033 4'-1 1/2" (PTP)
N33 3'-8 1/8"	N34 10'-4" (K)	N35 3'-7 1/2"
M21 5'-7"		M22 4'-7 1/2"
L21 4'-8 1/8"		L22 4'-7 1/2"
K21 5'-7"		K22 4'-7 1/2"
J21 4'-8 1/8"		J22 4'-7 1/2"
H21 5'-7"		H22 4'-7 1/2"
G21 4'-8 1/8"	FWD 8068	G22 4'-7 1/2"
F21 5'-7"		F22 4'-7 1/2"
E21 4'-8 1/8"		E22 4'-7 1/2"
D25 5'-7"		D26 4'-7 1/2"
C29 4'-8 1/8"		C30 4'-7 1/2"
B25 5'-7"		B26 4'-7 1/2"
A25 4'-8 1/8" (XX)		A26 4'-7 1/2" (XX)

B&G INS
CORNER PO

ELEVATION "F"

2 extra rows @ master bedroom wing
adjust height of plate cut in field to match

3 REQUIRED

model this area.

• Q4 4'-0" (PTP)	• Q5 6'-0" (PTP)	• Q6 6'-0" (PTP)	• Q7 3'-7 1/4" (PTP)
P4 6'-5 7/8"	P5 6'-7 1/2"	P6 6'-5 7/8"	
Q17 8'-4 3/4"	018 4'-7 1/2"	019 8'-4 3/4"	
(I) N17 6'-5 7/8"	• N18 6'-7 1/2" (K)	N19 6'-5 7/8"	
M12 8'-4 3/4"		M13 8'-4 3/4"	
(I) L12 7'-5 7/8"		L13 7'-5 7/8"	
K12 8'-4 3/4"		K13 8'-4 3/4"	
(I) J12 7'-5 7/8"		J13 7'-5 7/8"	
H12 8'-4 3/4"		H13 8'-4 3/4"	
(I) G12 7'-5 7/8"		G13 7'-5 7/8"	
F12 8'-4 3/4"		F13 8'-4 3/4"	
(I) E12 7'-5 7/8"		E13 7'-5 7/8"	
D13 7'-4 3/4"	D14 6'-7 1/2"	D15 7'-4 3/4"	
(I) C17 8'-0"	C18 7'-0"	C19 4'-7 1/4"	
B13 4'-0"		B15 8'-0"	
(I) B14 6'-0"		B16 3'-5"	
• A14 6'-6" (XX)	• A15 6'-0" (XX)	• A16 7'-1 1/4" (XX)	

ELEVATION "D"

6x6
CORN

• 034 5'-3 1/2" (PTP)	• 035 6'-0" (PTP)	• 036 4'-10" (PTP)
• N36 4'-9 1/2" (K)	N37 8'-0"	N38 3'-4"
N23 1'-3 1/2"	N24 6'-0"	N25 6'-4"
L23 1'-3 1/2"	L24 8'-0"	L25 4'-4"
K23 1'-3 1/2"	K24 5'-0"	K25 7'-4"
J23 1'-3 3'-2 1/8"	J24 7'-0"	J25 5'-4"
H23 1'-3 1/2"	H24 4'-0"	H25 8'-4"
C23 1'-3 1/2"	G24 6'-0"	G25 6'-4"
F23 1'-3 1/2"	F24 8'-0"	E25 4'-4"
E23 4'-9 1/2"	E24 4'-0"	E25 7'-4"
D27 7'-0"	D28 6'-0"	D29 3'-2"
C31 4'-0"	C32 6'-0"	C33 6'-2"
B27 8'-0"	B28 8'-2"	
• A27 6'-0" (XX)	• A28 6'-0" (XX)	• A29 4'-2" (XX)

6" added to length
of these logs.

ELEVATION "G"


KATAHDIN F
PC
OAKFIE
I-8
EAV

APPROVED W
APPROVED BY
DATE

C1 CH
 C2 CN
 P1 CM
 OTHER

THESE PLANS ARE PROVIDED FOR INFORMATION ONLY / OR REVISIONS. PLEASE REVIEW AND APPROVE THESE PLANS THOROUGHLY. A SIGNATURE OF APPROVAL IS REQUIRED ON THE STANDBY FOREST PLAN. ADDITIONAL DRAWINGS MAY BE SUBMITTED FOR APPROVAL DRAFTER APPROVAL DRAWINGS. NO CHANGES OR MODIFICATIONS ARE ALLOWED WITHOUT APPROVAL. ADDITIONAL COSTS ARE NOT ALLOWED.

CUSTOMER:	FORREST
TITLE:	LOG ELEVATOR
DATE:	5-1-01
DRAWN BY:	JL
PLAN #	01043803

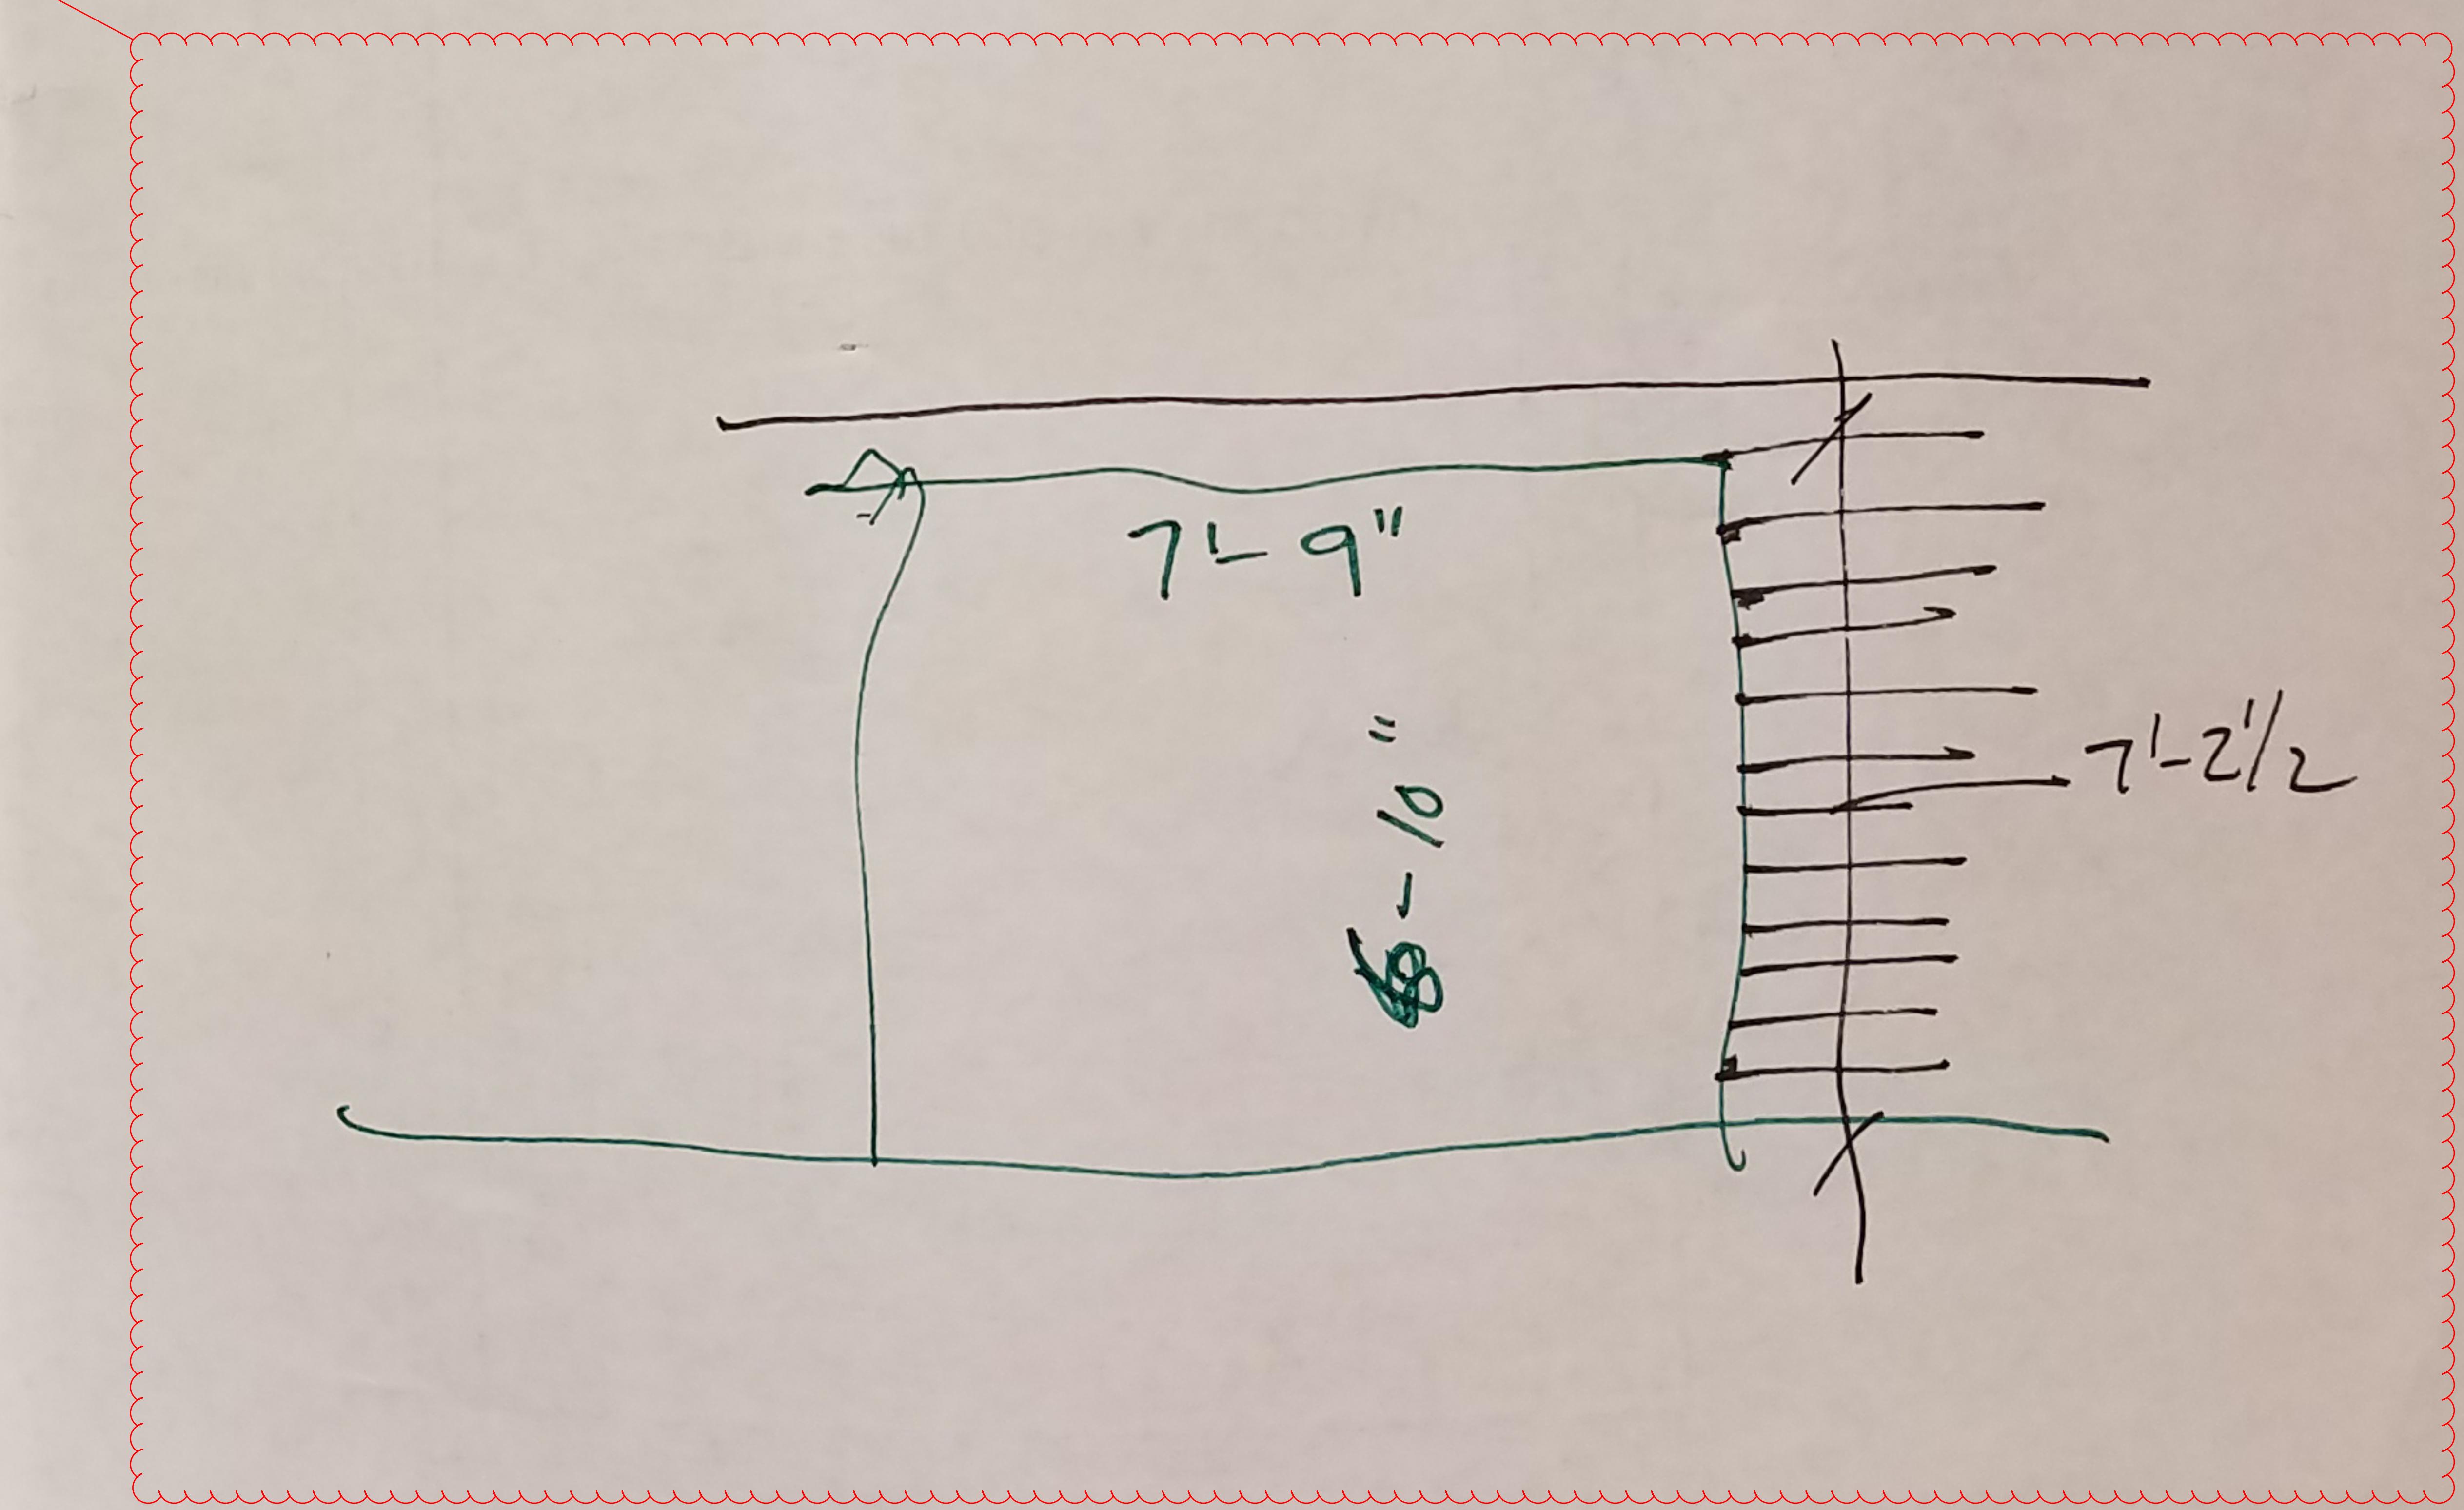

elevation
of
opening

7'-9"

6'-10"

7'-2 1/2"